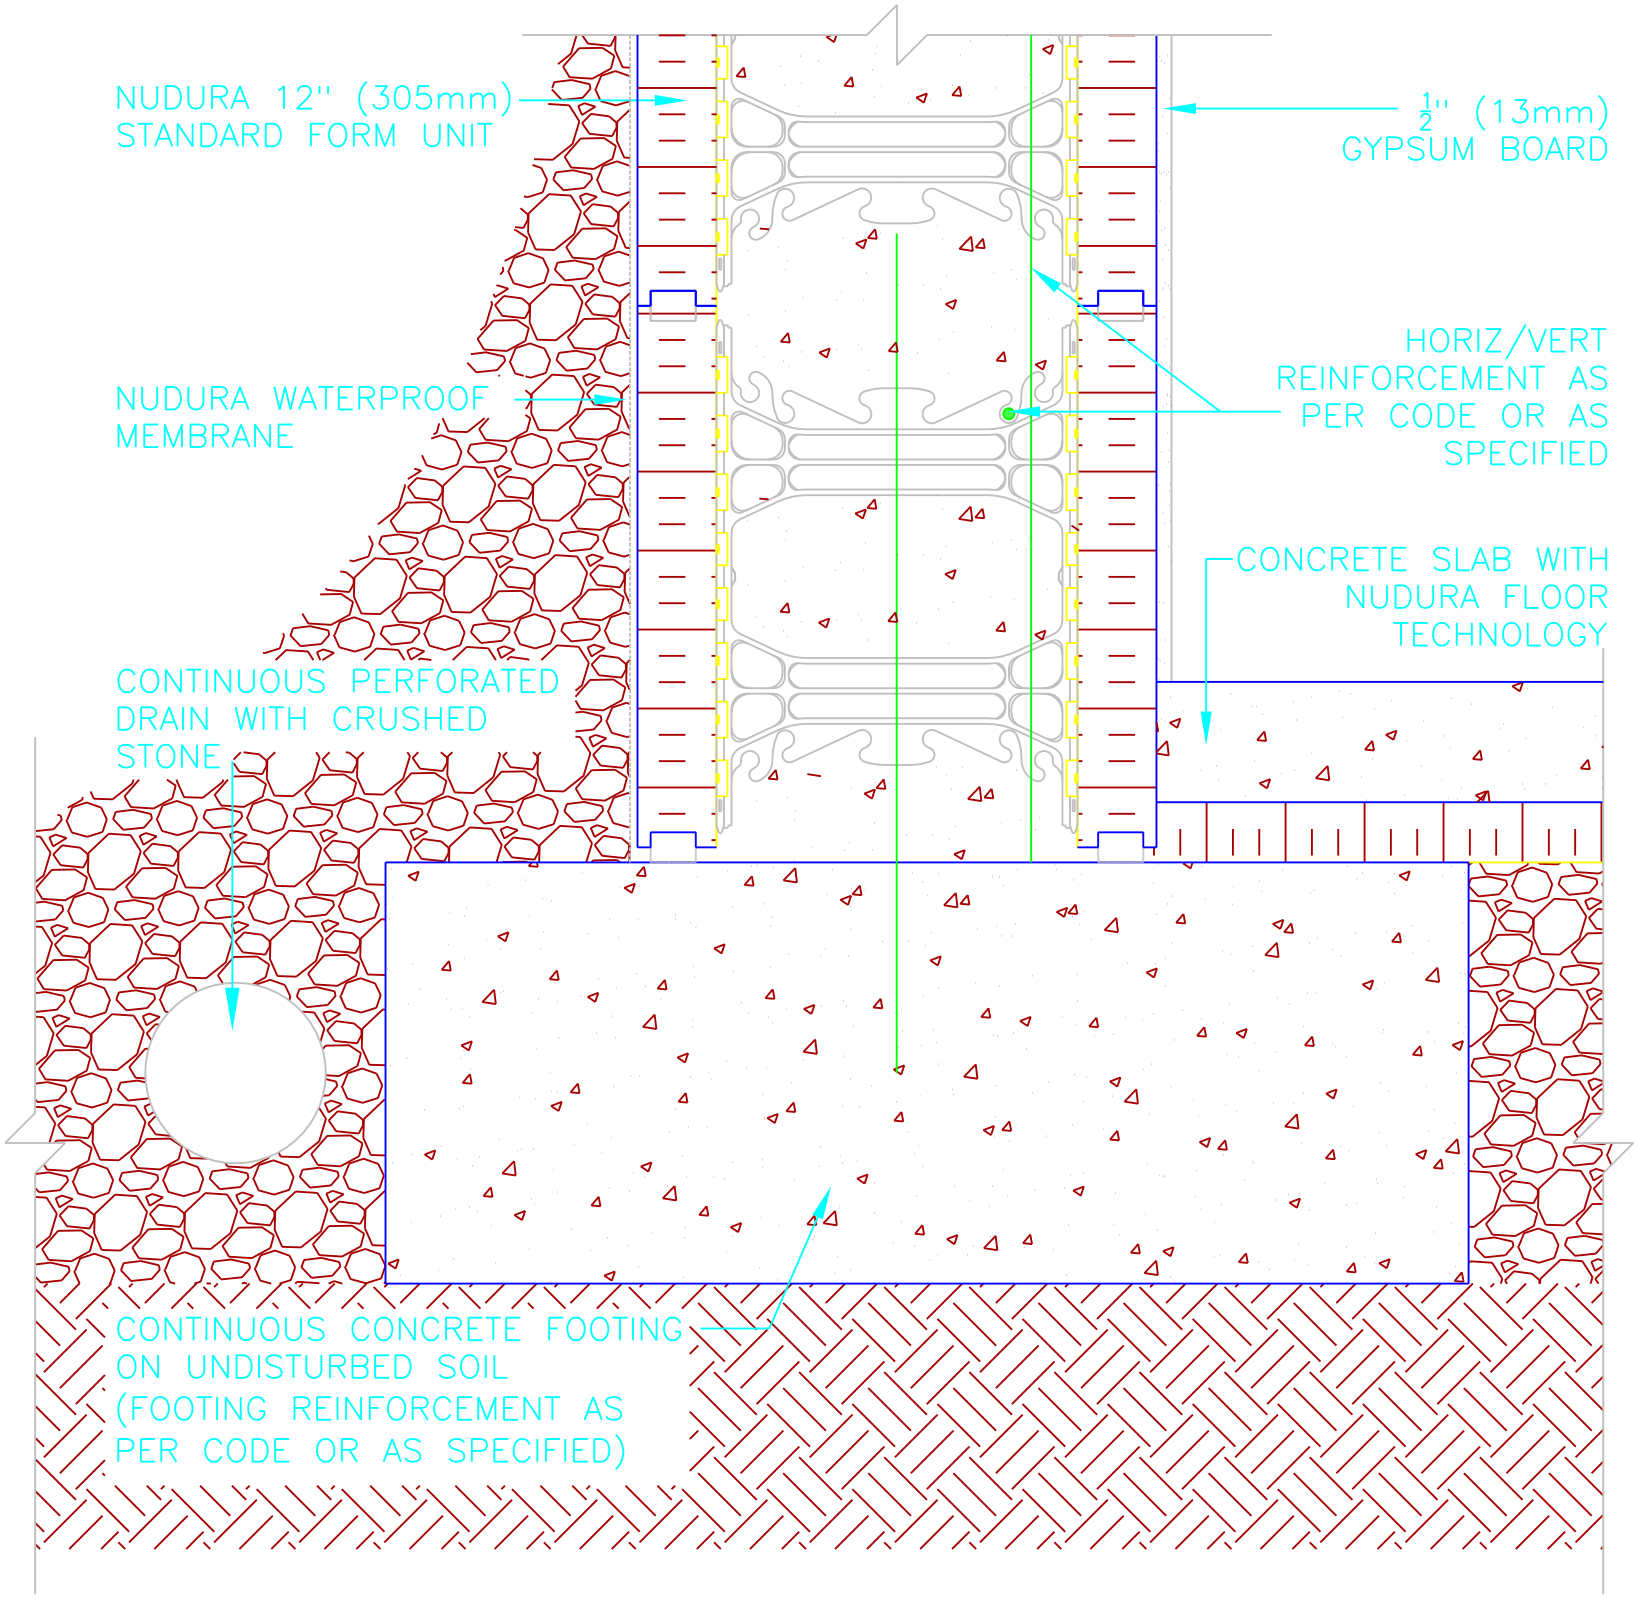
NUDURA 12" (305mm)
STANDARD FORM UNIT
½" (13mm)
GYPSUM BOARD
HORIZ/VERT
REINFORCEMENT AS
PER CODE OR AS
SPECIFIED
NUDURA WATERPROOF
MEMBRANE
CONCRETE SLAB WITH
NUDURA FLOOR
TECHNOLOGY
CONTINUOUS PERFORATED
DRAIN WITH CRUSHED
STONE
CONTINUOUS CONCRETE FOOTING
ON UNDISTURBED SOIL
(FOOTING REINFORCEMENT AS
PER CODE OR AS SPECIFIED)

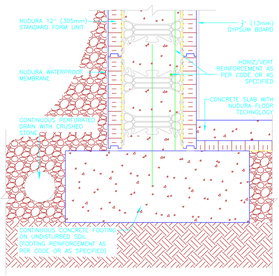

DIAGRAMS INDICATE GENERAL INFORMATION REQUIRED FOR COMPLIANCE WITH NUDURA FLOOR TECHNOLOGY. ADJUST AS THE REQUIRED BY THE DESIGNER

NUDURA
INTEGRATED BUILDING TECHNOLOGY
Building Value.

NUDURA 12" (305mm) FOAM UNIT
NUDURA FLOOR TECHNOLOGY
STRIP FOOTING DETAIL

REV. NO.	DWG NO.
REV. DATE	312A02
2013	
DRAWN BY: CRA	SCALE 0